
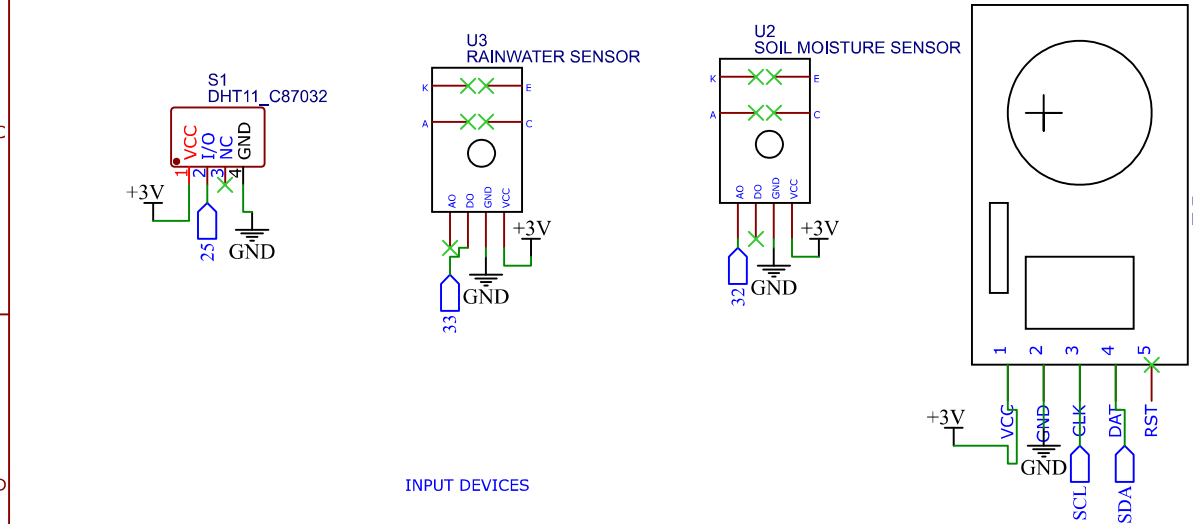


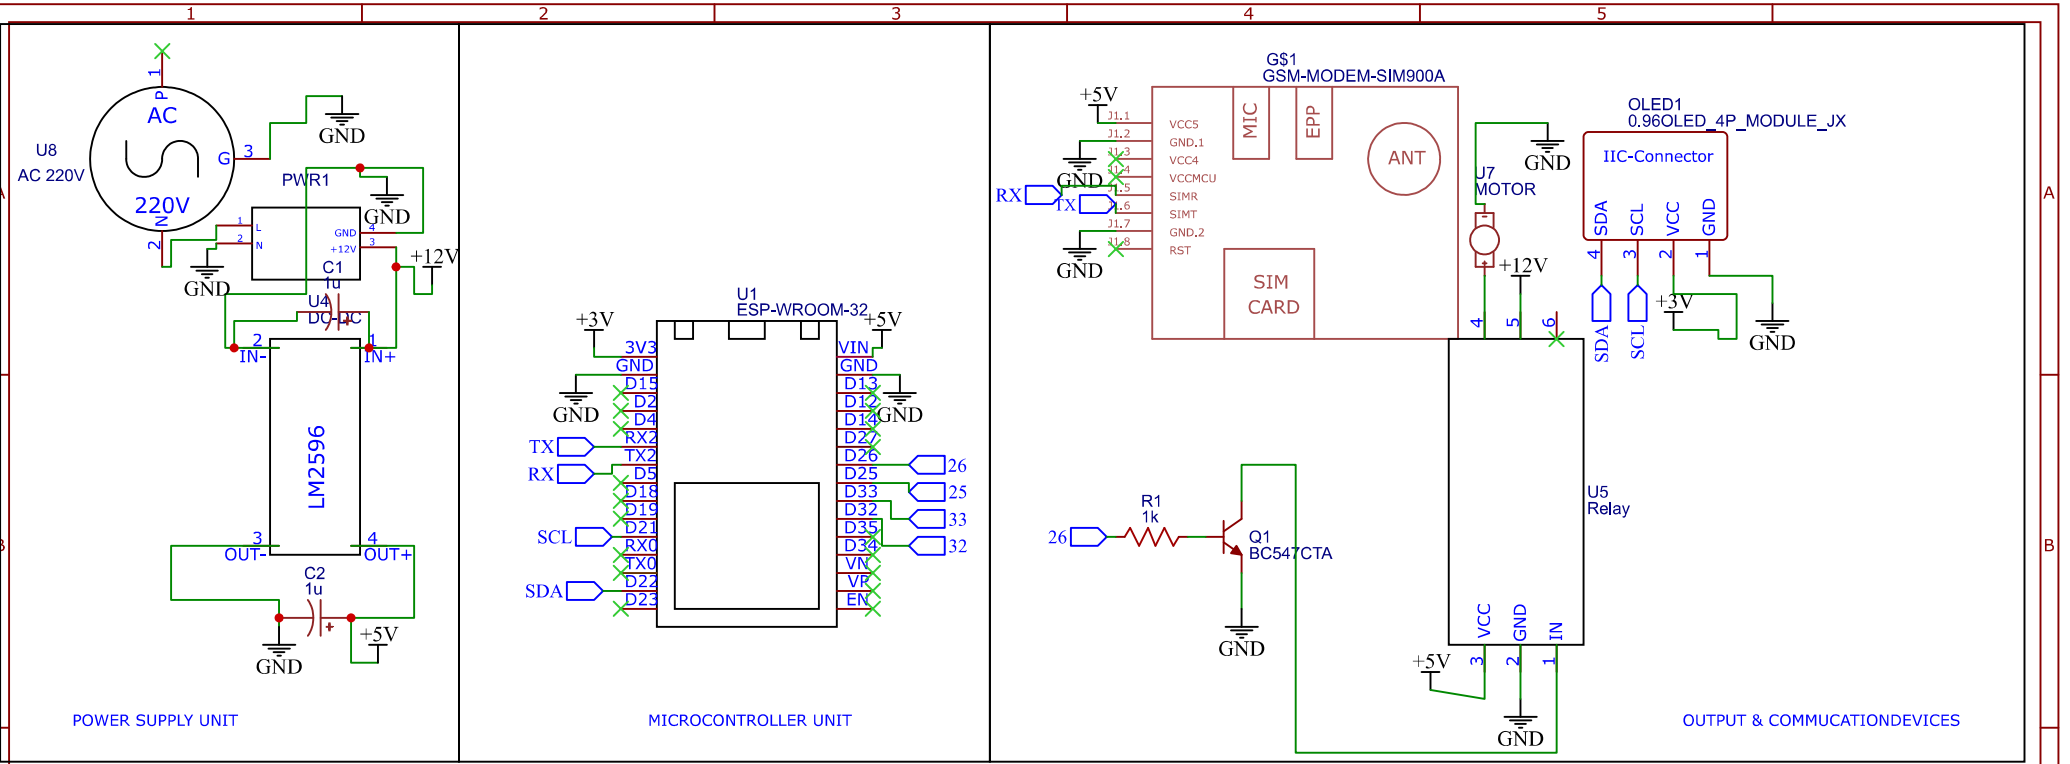

TITLE: IPL PROJECT		REV: 1.0
Company: KVG E&C DEPT		Sheet: 1/1
Date: 2026-05-17		Drawn By: H GOPALAKRISHNA PRABHU